


PLAN OF SUBDIVISION				EDITION 1		PS 912610 M	
LOCATION OF LAND PARISH: Nar Nar Goon TOWNSHIP: --- SECTION: --- CROWN ALLOTMENT: --- CROWN PORTION: 43 (Pt) TITLE REFERENCE: Vol. 7712 Fol. 050 LAST PLAN REFERENCE: Lot 48 Block E on LP 3022 POSTAL ADDRESS: 25 Princes Highway, PAKENHAM 3810 (at time of subdivision) MGA CO-ORDINATES: E: 367 040 ZONE: 55 (of approx centre of land N: 5 785 060 GDA 2020 in plan)				Council Name: Cardinia Shire Council			
VESTING OF ROADS AND/OR RESERVES				NOTATIONS			
IDENTIFIER		COUNCIL/BODY/PERSON		Building Boundaries are defined by thick continuous lines. Location of Boundaries defined by Buildings Median : Denoted thus 'M' Exterior Face of Wall: All other Boundaries Boundaries marked '*' are defined by a projection of the median/exterior face of wall at the ground floor. LOTS IN THIS PLAN MAY BE AFFECTED BY ONE OR MORE OWNERS CORPORATIONS. FOR DETAILS OF ANY OWNERS CORPORATIONS INCLUDING PURPOSE, RESPONSIBILITY, OR ENTITLEMENT & LIABILITY SEE OWNERS CORPORATION SEARCH REPORT, OWNERS CORPORATION ADDITIONAL INFORMATION AND IF APPLICABLE, OWNERS CORPORATION RULES.			
Nil		Nil					
NOTATIONS							
DEPTH LIMITATION: DOES NOT APPLY							
SURVEY: This plan is based on survey. STAGING: This is not a staged subdivision. Planning Permit No. T220530 This survey has been connected to permanent marks No(s). 73 & 109. In Proclaimed Survey Area No. 71							
EASEMENT INFORMATION							
LEGEND: A - Appurtenant Easement E - Encumbering Easement R - Encumbering Easement (Road)							
Easements and rights implied by Section 12(2) of the Subdivision Act 1988 apply to all of the land in this plan.							
Easement Reference	Purpose	Width (Metres)	Origin	Land Benefited/In Favour Of			
E-1	Sewerage	2.80	This Plan	South East Water Corporation			
NOBELIUS LAND SURVEYORS		SURVEYORS FILE REF: 20665		ORIGINAL SHEET SIZE: A3	SHEET 1 OF 3		
P.O. BOX 461 PAKENHAM 3810 Ph 03 5941 4112 mail@nobelius.com.au		LICENSED SURVEYOR: T. D. WALKER		VERSION A			

DIAGRAM 1
GROUND FLOOR

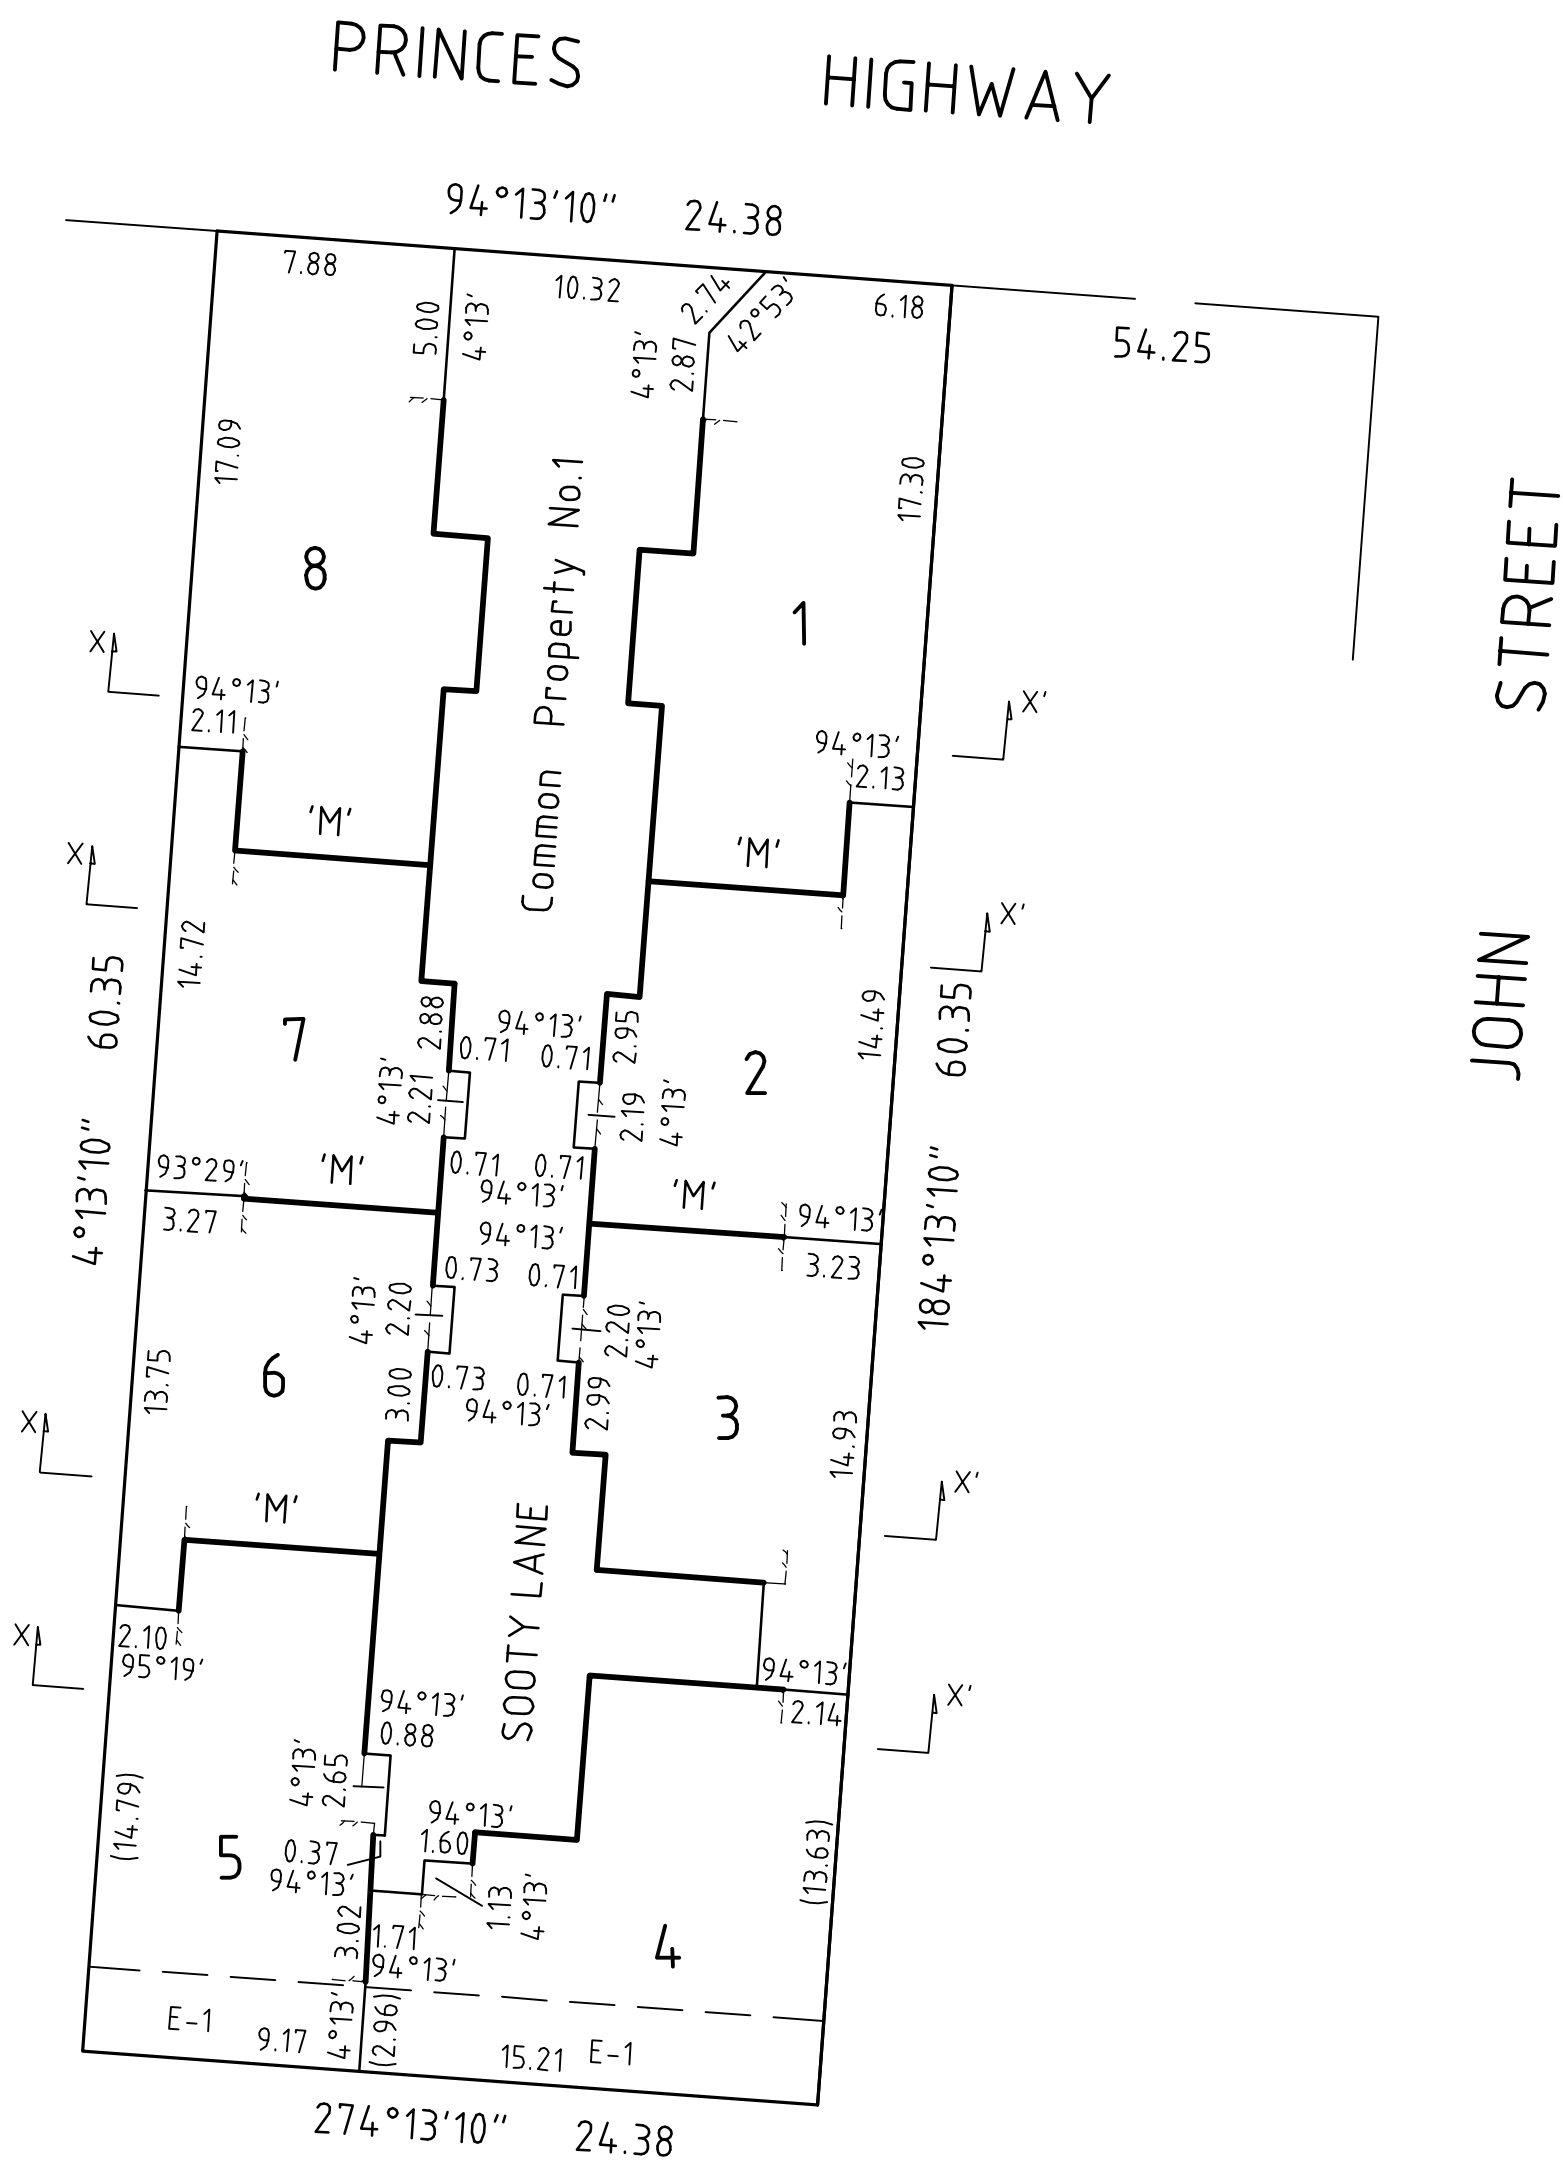


NOBELIUS LAND SURVEYORS



P.O. BOX 461
PAKENHAM 3810
Ph 03 5941 4112
mail@nobelius.com.au

SCALE
1:250


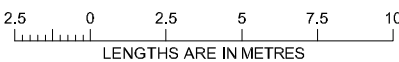


LICENSED SURVEYOR: T. D. WALKER
VERSION A

ORIGINAL SHEET
SIZE: A3

SHEET 2

DIAGRAM 2
FIRST FLOOR

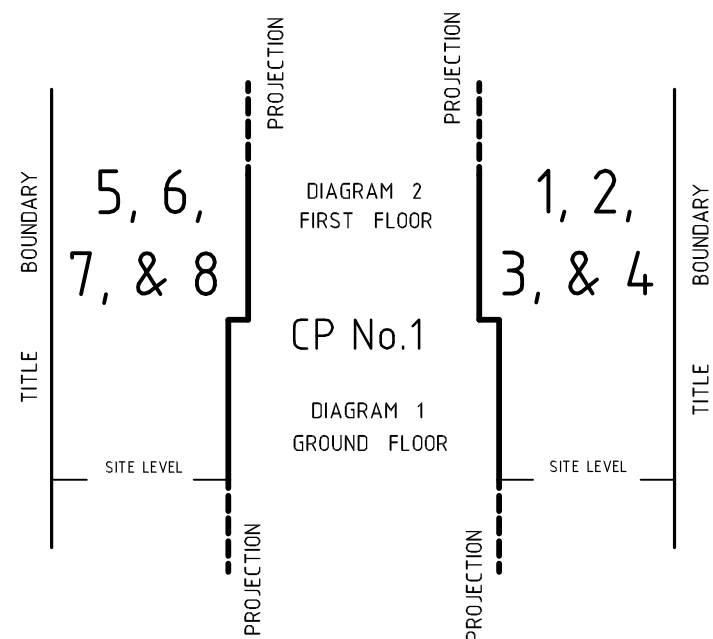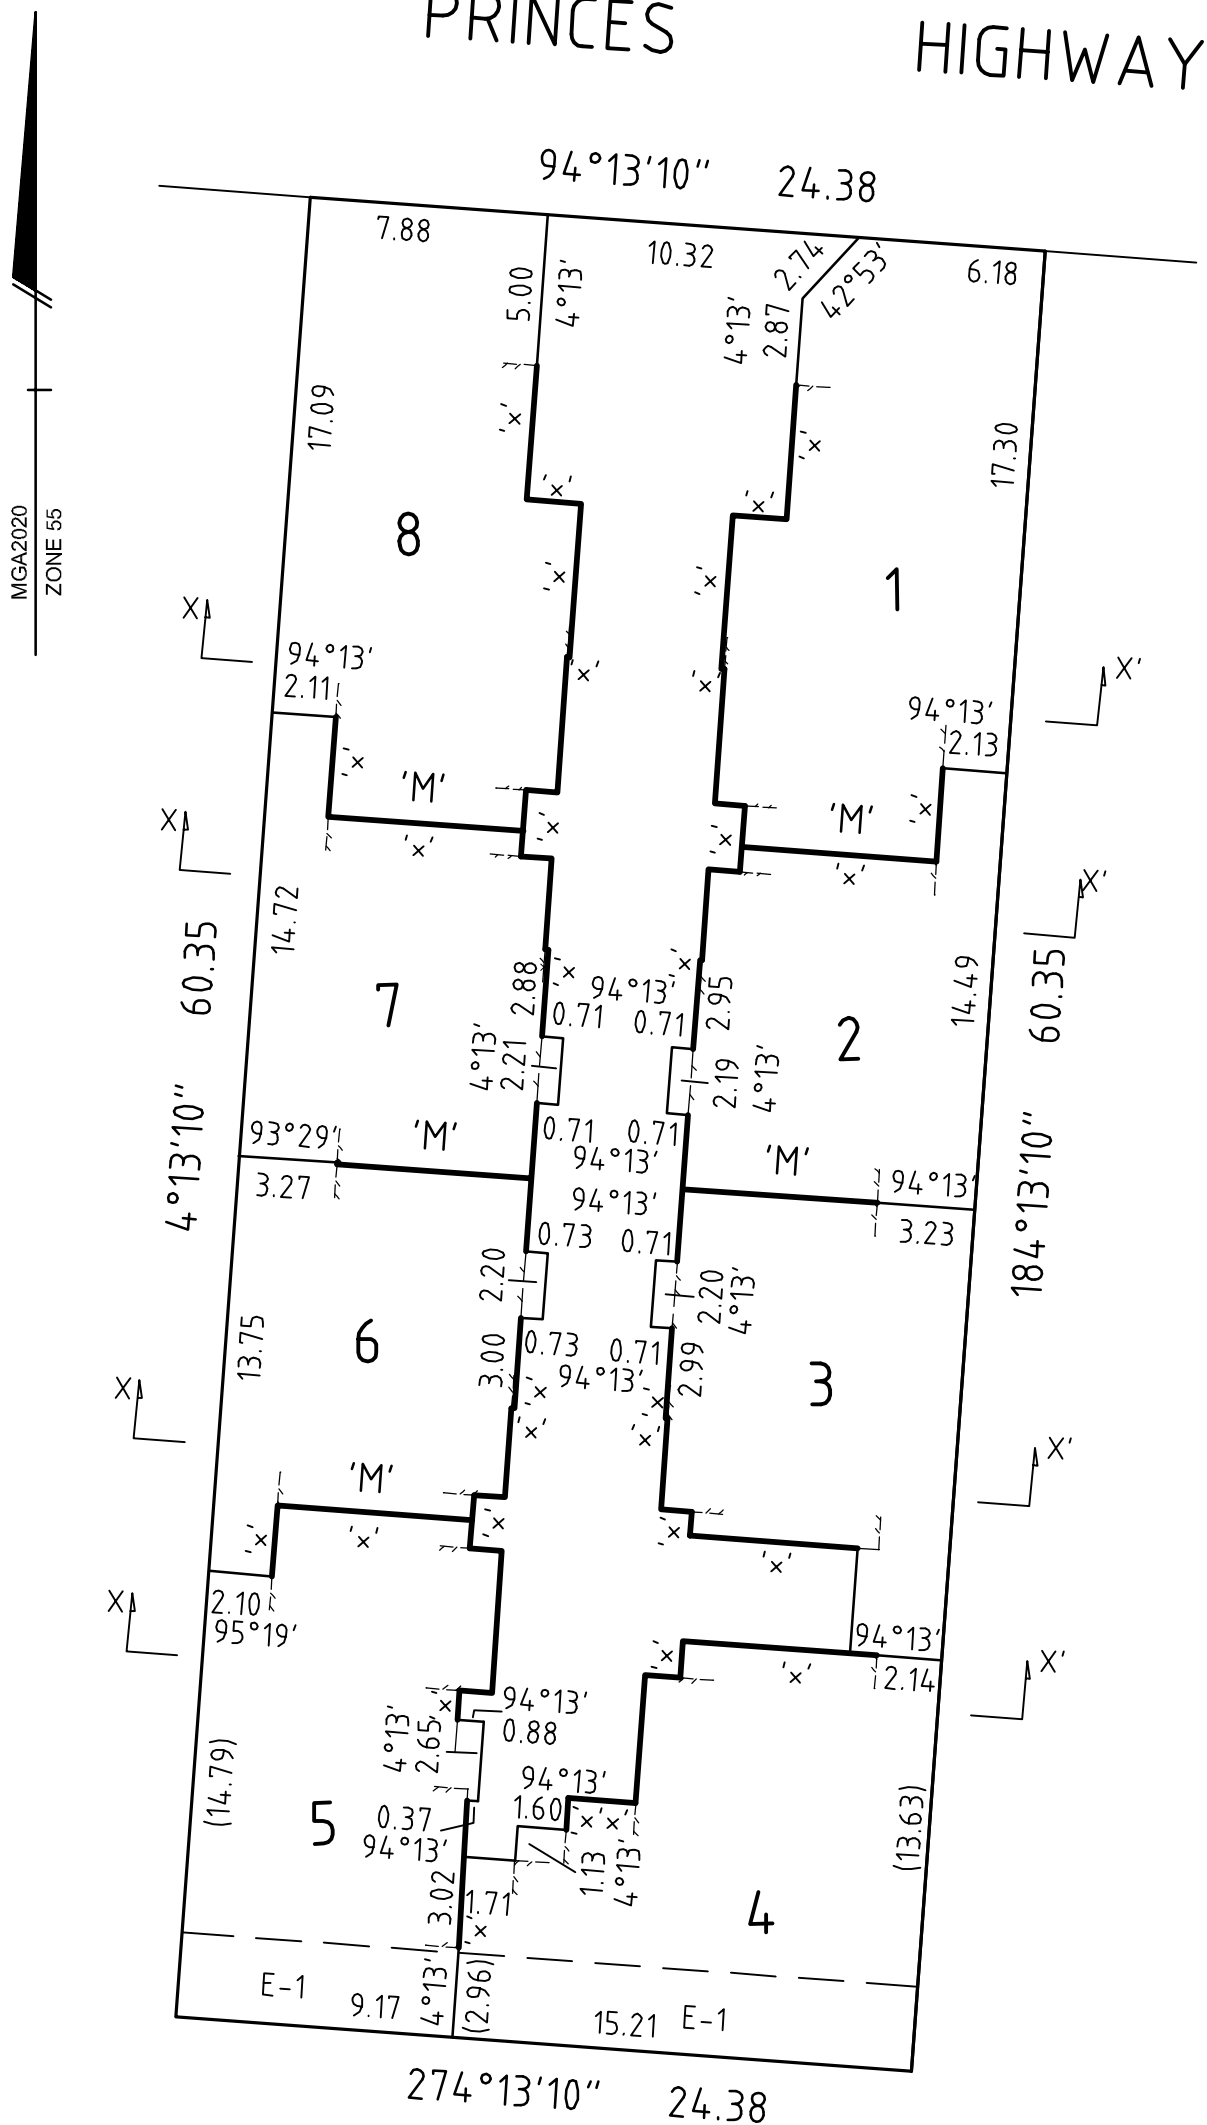


TYPICAL FOR ALL LOTS
SECTION X - X'
Not to Scale

NOBELIUS LAND SURVEYORS



P.O. BOX 461
PAKENHAM 3810
Ph 03 5941 4112
mail@nobelius.com.au

SCALE
1:250

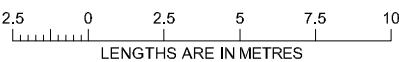

LICENSED SURVEYOR: T. D. WALKER
VERSION A

ORIGINAL SHEET
SIZE: A3

SHEET 3

OWNERS CORPORATION SCHEDULE

PS912610M

Owners Corporation No.

1

Plan No.

PS912610M

Land affected by Owners Corporation

Lots: ALL OF THE LOTS IN THE TABLE BELOW

Common Property No.:

Limitations of Owners Corporation:

UNLIMITED

Notations

Totals		
	Entitlement	Liability
This schedule	400	400
Previous stages	0	0
Overall Total	400	400

Lot Entitlement and Lot Liability

Lot	Entitlement	Liability
1	50	50
2	50	50
3	50	50
4	50	50
5	50	50
6	50	50
7	50	50
8	50	50

NOBELIUS LAND SURVEYORS



P.O. BOX 461
PAKENHAM 3810
Ph 03 5941 4112
mail@nobelius.com.au

SURVEYORS FILE REFERENCE: 20665

SHEET 1 of 1

ORIGINAL SHEET
SIZE: A3

Licensed Surveyor: T. D. WALKER VERSION A