


PLAN OF SUBDIVISION				EDITION 1		PS 932352U	
LOCATION OF LAND PARISH: DANDENONG TOWNSHIP: – SECTION: – CROWN ALLOTMENT: – CROWN PORTION: 46 (PART) TITLE REFERENCES: VOL 8258 FOL 070 VOL 8258 FOL 073 LAST PLAN REFERENCE/S: LOTS 2 AND 3 LP 43926 POSTAL ADDRESS: 14 GRACE AVENUE (At time of subdivision) DANDENONG 3175 MGA2020 COORDINATES E 343 946 (of approx centre of land N 5 794 797 in plan) ZONE: 55				Council Name: City of Greater Dandenong SPEAR Reference Number: S249135H			
VESTING OF ROADS AND/OR RESERVES				NOTATIONS			
IDENTIFIER		COUNCIL/BODY/PERSON		DEPTH LIMITATION: Does not apply BOUNDARIES DEFINED BY BUILDINGS ARE SHOWN BY THICK CONTINUOUS LINES. LOCATION OF BOUNDARIES DEFINED BY BUILDINGS: MEDIAN: BOUNDARY SHOWN "M" EXTERIOR FACE: ALL OTHER BOUNDARIES LOTS ON THIS PLAN MAY BE AFFECTED BY ONE OR MORE OWNERS CORPORATIONS. FOR DETAILS OF ANY OWNERS CORPORATIONS INCLUDING PURPOSE, RESPONSIBILITY, ENTITLEMENT AND LIABILITY SEE OWNERS CORPORATION ADDITIONAL INFORMATION AND IF APPLICABLE OWNERS CORPORATION RULES.			
NIL		NIL					
NOTATIONS				STAGING: This is/is not a staged subdivision			
SURVEY: This plan is/is not based on survey.							
EASEMENT INFORMATION							
LEGEND A–Appurtenant Easement E–Encumbering Easement R–Encumbering Easement (Road)							
Section 12(2) of the Subdivision Act 1988 applies to the whole of this plan							
Easement Reference	Purpose	Width (Metres)	Origin	Land Benefited/In Favour Of			
E–1	SEWERAGE	2.10	THIS PLAN	SOUTH EAST WATER CORPORATION			
M. J. Reddie Surveys Pty Ltd ABN 49 005 965 257 1 Horner Street, Beaconsfield. 3807 P.O. Box 268, Berwick. 3806 Phone (03) 9707 4117 Fax (03) 9707 4428		REF: 25–02–388		FILE: 603601		ORIGINAL SHEET SIZE: A3	SHEET 1 OF 2
		Digitally signed by: Michael J Reddie, Licensed Surveyor, Surveyor's Plan Version (3), 10/02/2026, SPEAR Ref: S249135H					

GRACE AVENUE

STUD ROAD

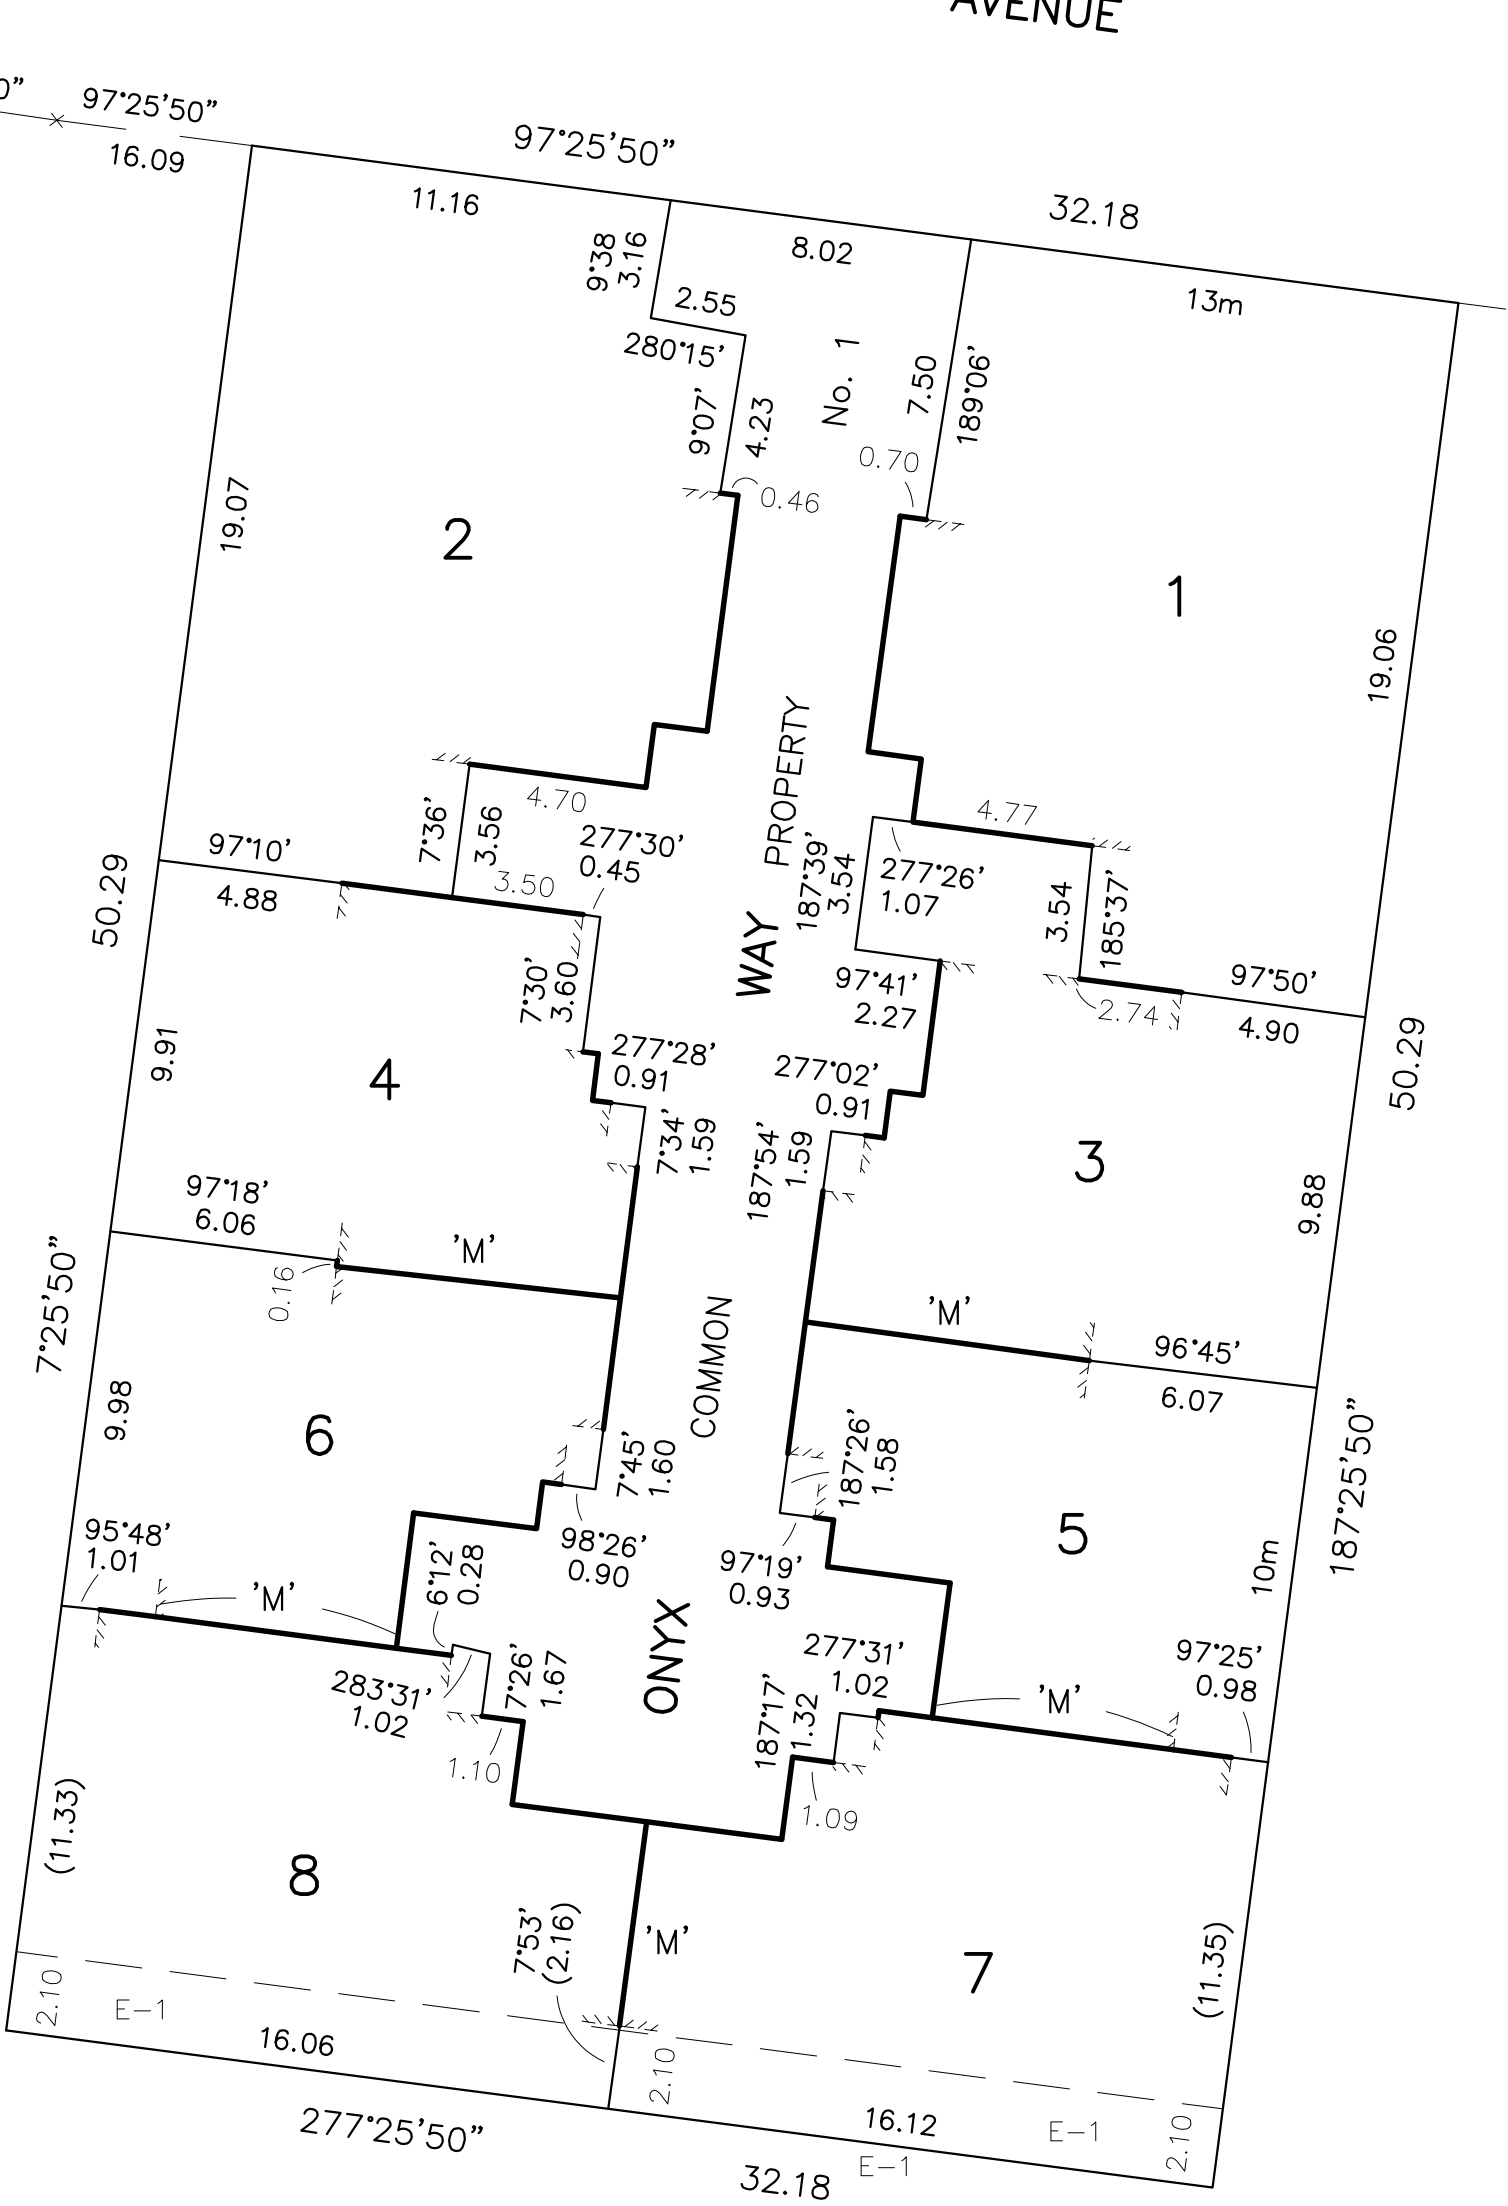

M. J. Reddie Surveys Pty Ltd

ABN 49 005 965 257

1 Horner Street, Beaconsfield. 3807

P.O. Box 268, Berwick. 3806

Phone (03) 9707 4117 Fax (03) 9707 4428

SCALE
1:200



LENGTHS ARE IN METRES

Digitally signed by: Michael J Reddie, Licensed Surveyor,
Surveyor's Plan Version (3),
10/02/2026, SPEAR Ref: S249135H

ORIGINAL SHEET
SIZE : A3

SHEET 2

OWNERS CORPORATION SCHEDULE

PS932352U

Owners Corporation No. 1	Plan No. PS932352U
--------------------------	--------------------

Plan No. PS932352U

Land affected by Owners Corporation:	LOTS 1 TO 8
--------------------------------------	-------------

Common Property No.: 1

Limitations of Owners Corporation:	Unlimited
------------------------------------	-----------

Totals		
	Entitlement	Liability
This schedule	80	80
Balance of existing OC	0	0
Overall Total	80	80

Totals		
	Entitlement	Liability
This schedule	80	80
Balance of existing OC	0	0
Overall Total	80	80

Lot Entitlement and Lot Liability

[illegible]

M.J.Reddie Surveys Pty Ltd
1 Horner Street Beaconsfield VIC 3807

SURVEYORS FILE REFERENCE: 25-02-388

SHEET 1

ORIGINAL SHEET
SIZE: A3

Digitally signed by: Michael J Reddie, Licensed Surveyor,
Surveyor's Plan Version (3),
10/02/2026, SPEAR Ref: S249135H